

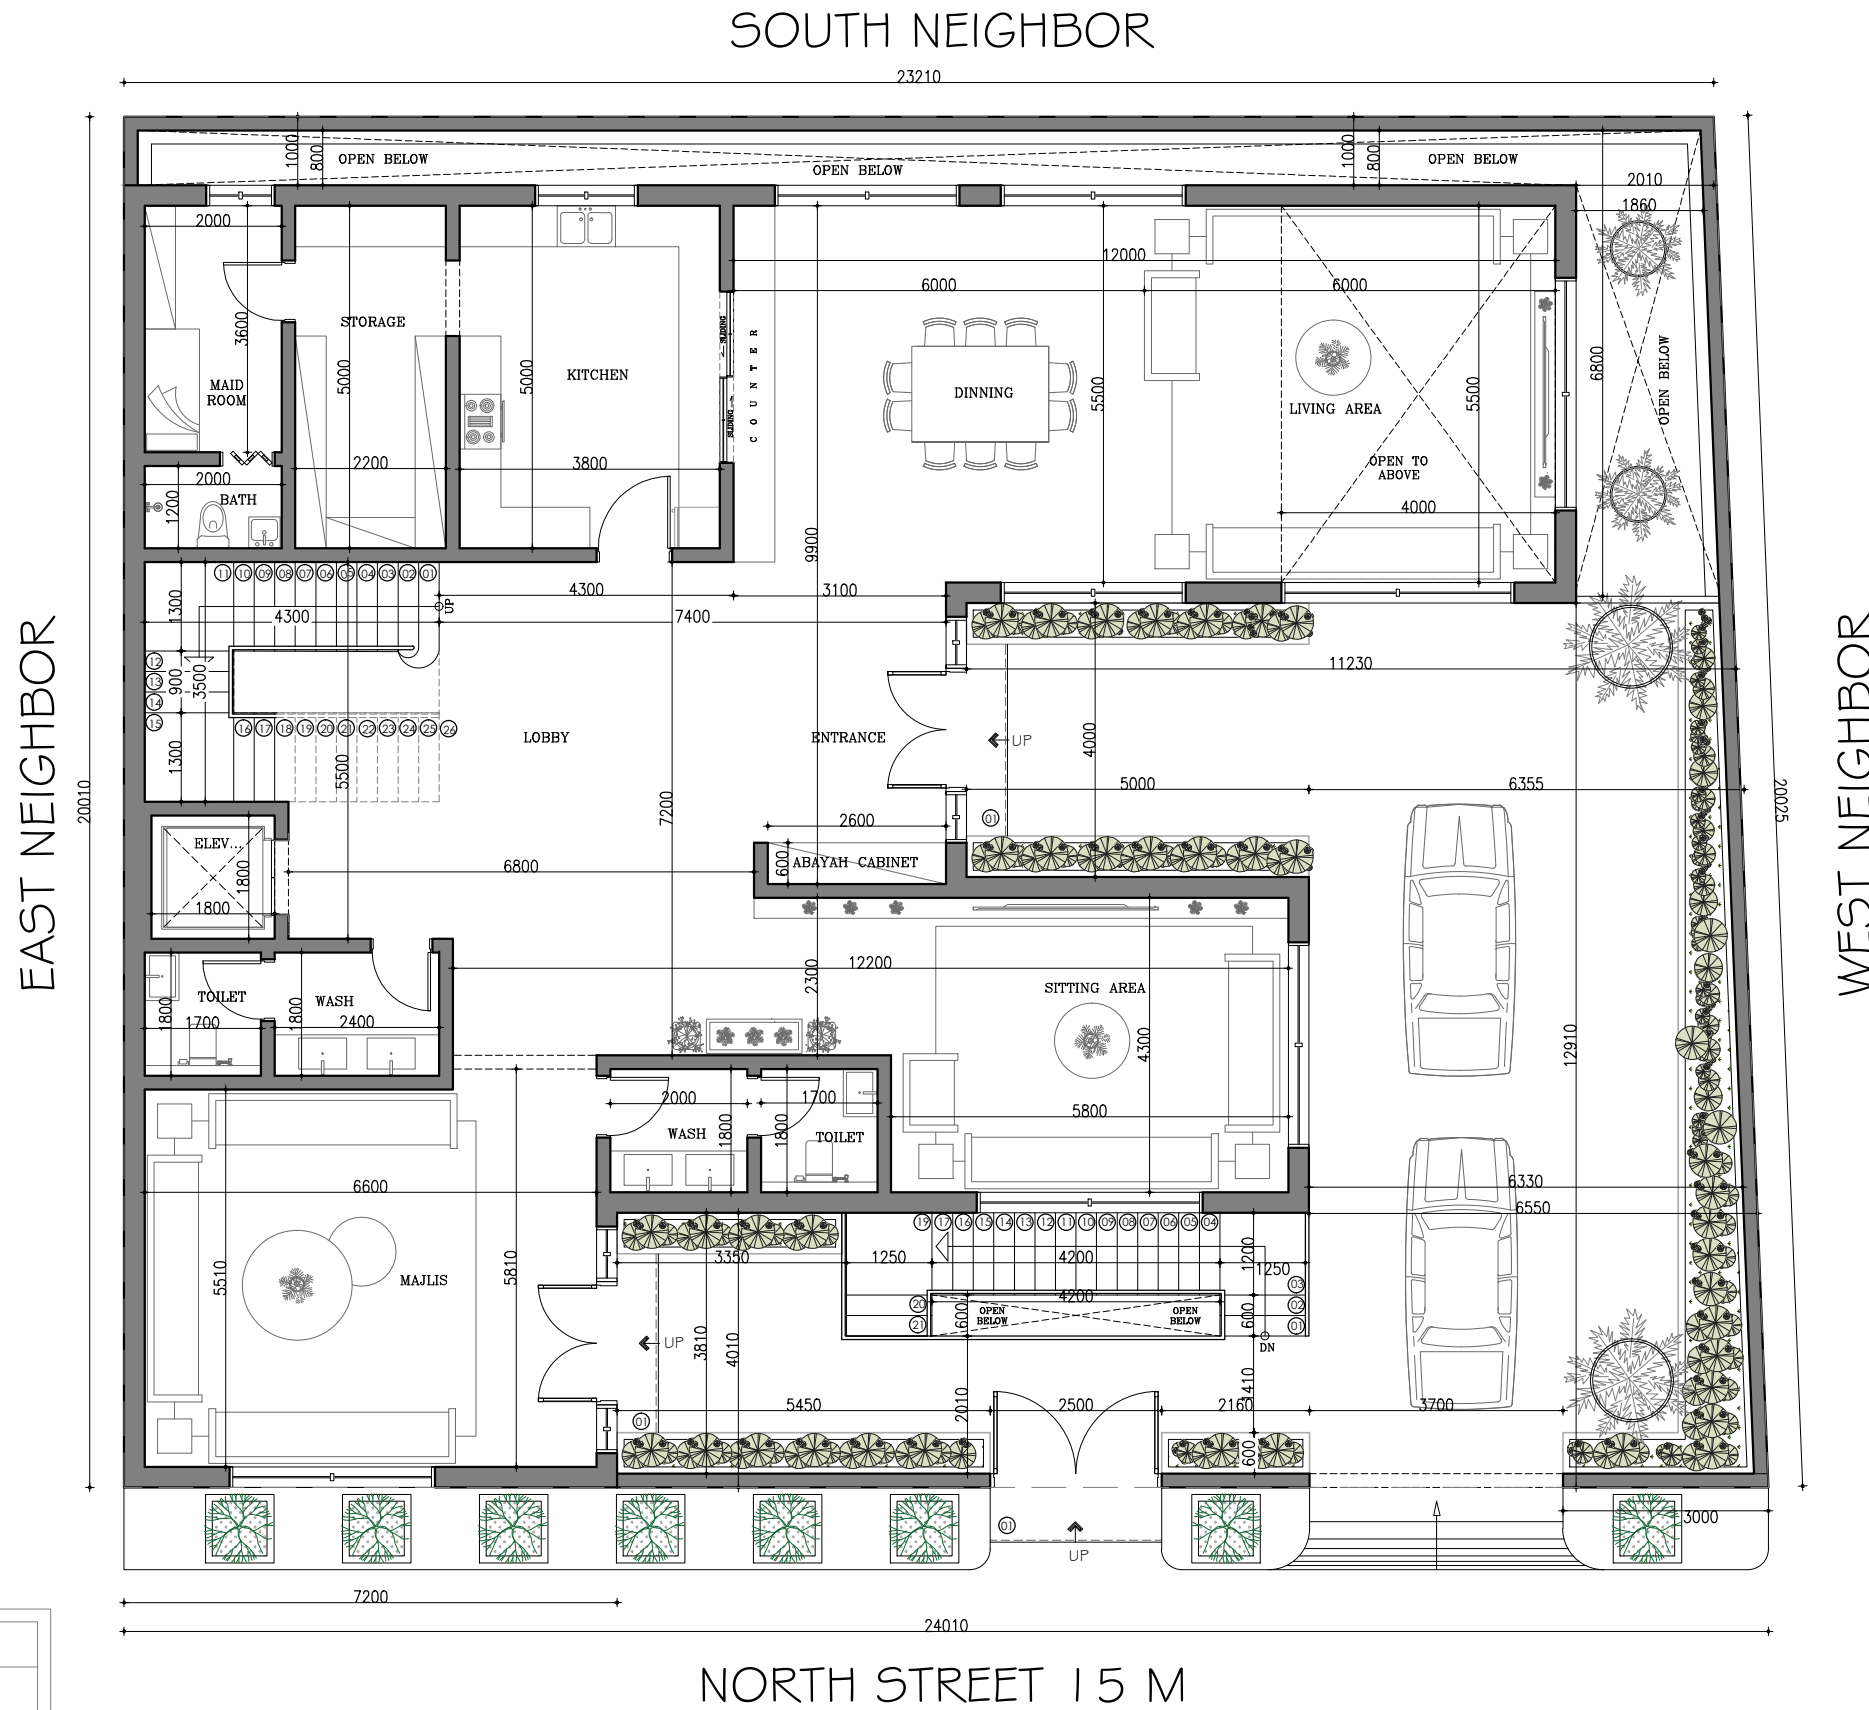


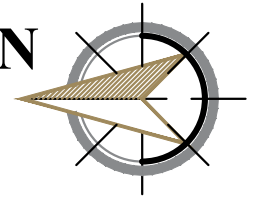

TOTAL LOT AREA =472.40 SQM		
GROUND FLOOR	AREA = 292.1 SQM	PERCENTAGE 61.83 %
BASEMENT FLOOR	369.1 SQM	78.13 %
FIRST FLOOR		
ROOF FLOOR		

GROUND FLOOR PLAN

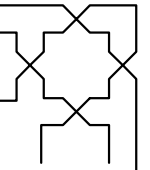

مالك المشروع:

عنوان المشروع:

فيلا سكنية

عنوان اللوحة:

المصمم:

ارينا للاستشارات الهندسية

المراجعة:

ارينا للاستشارات الهندسية

موقع المشروع:

الرياض-

المقياس:

N.T.S

رمز المشروع:


B2660

التاريخ:

يونيو 2026


رقم الصفحة:


001

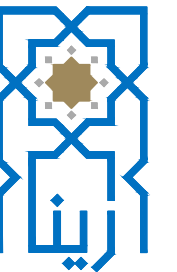


ARENA
ARCHITECTURE
www.arenaarch.sa

مكتب ارينا للاستشارات الهندسية ٣٨٨
حو. الملك طريق اس بن مالك مكتب رقم ١٢
الرياض ١١٥٣٧ المملكة العربية السعودية
هاتف ٣٧١٥-٤٣٣٣٢٢ فاكس ١١-٤٣٣٣١٤١
جوال ٥٥٧٠٧٣٣٣٦ بريد الكتروني info@arenaarch.sa

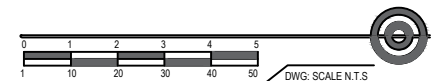

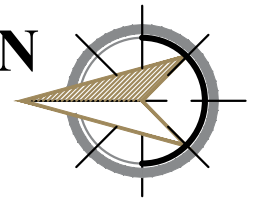


01

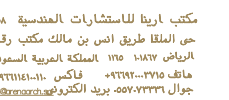

EAST NEIGHBOR

23210

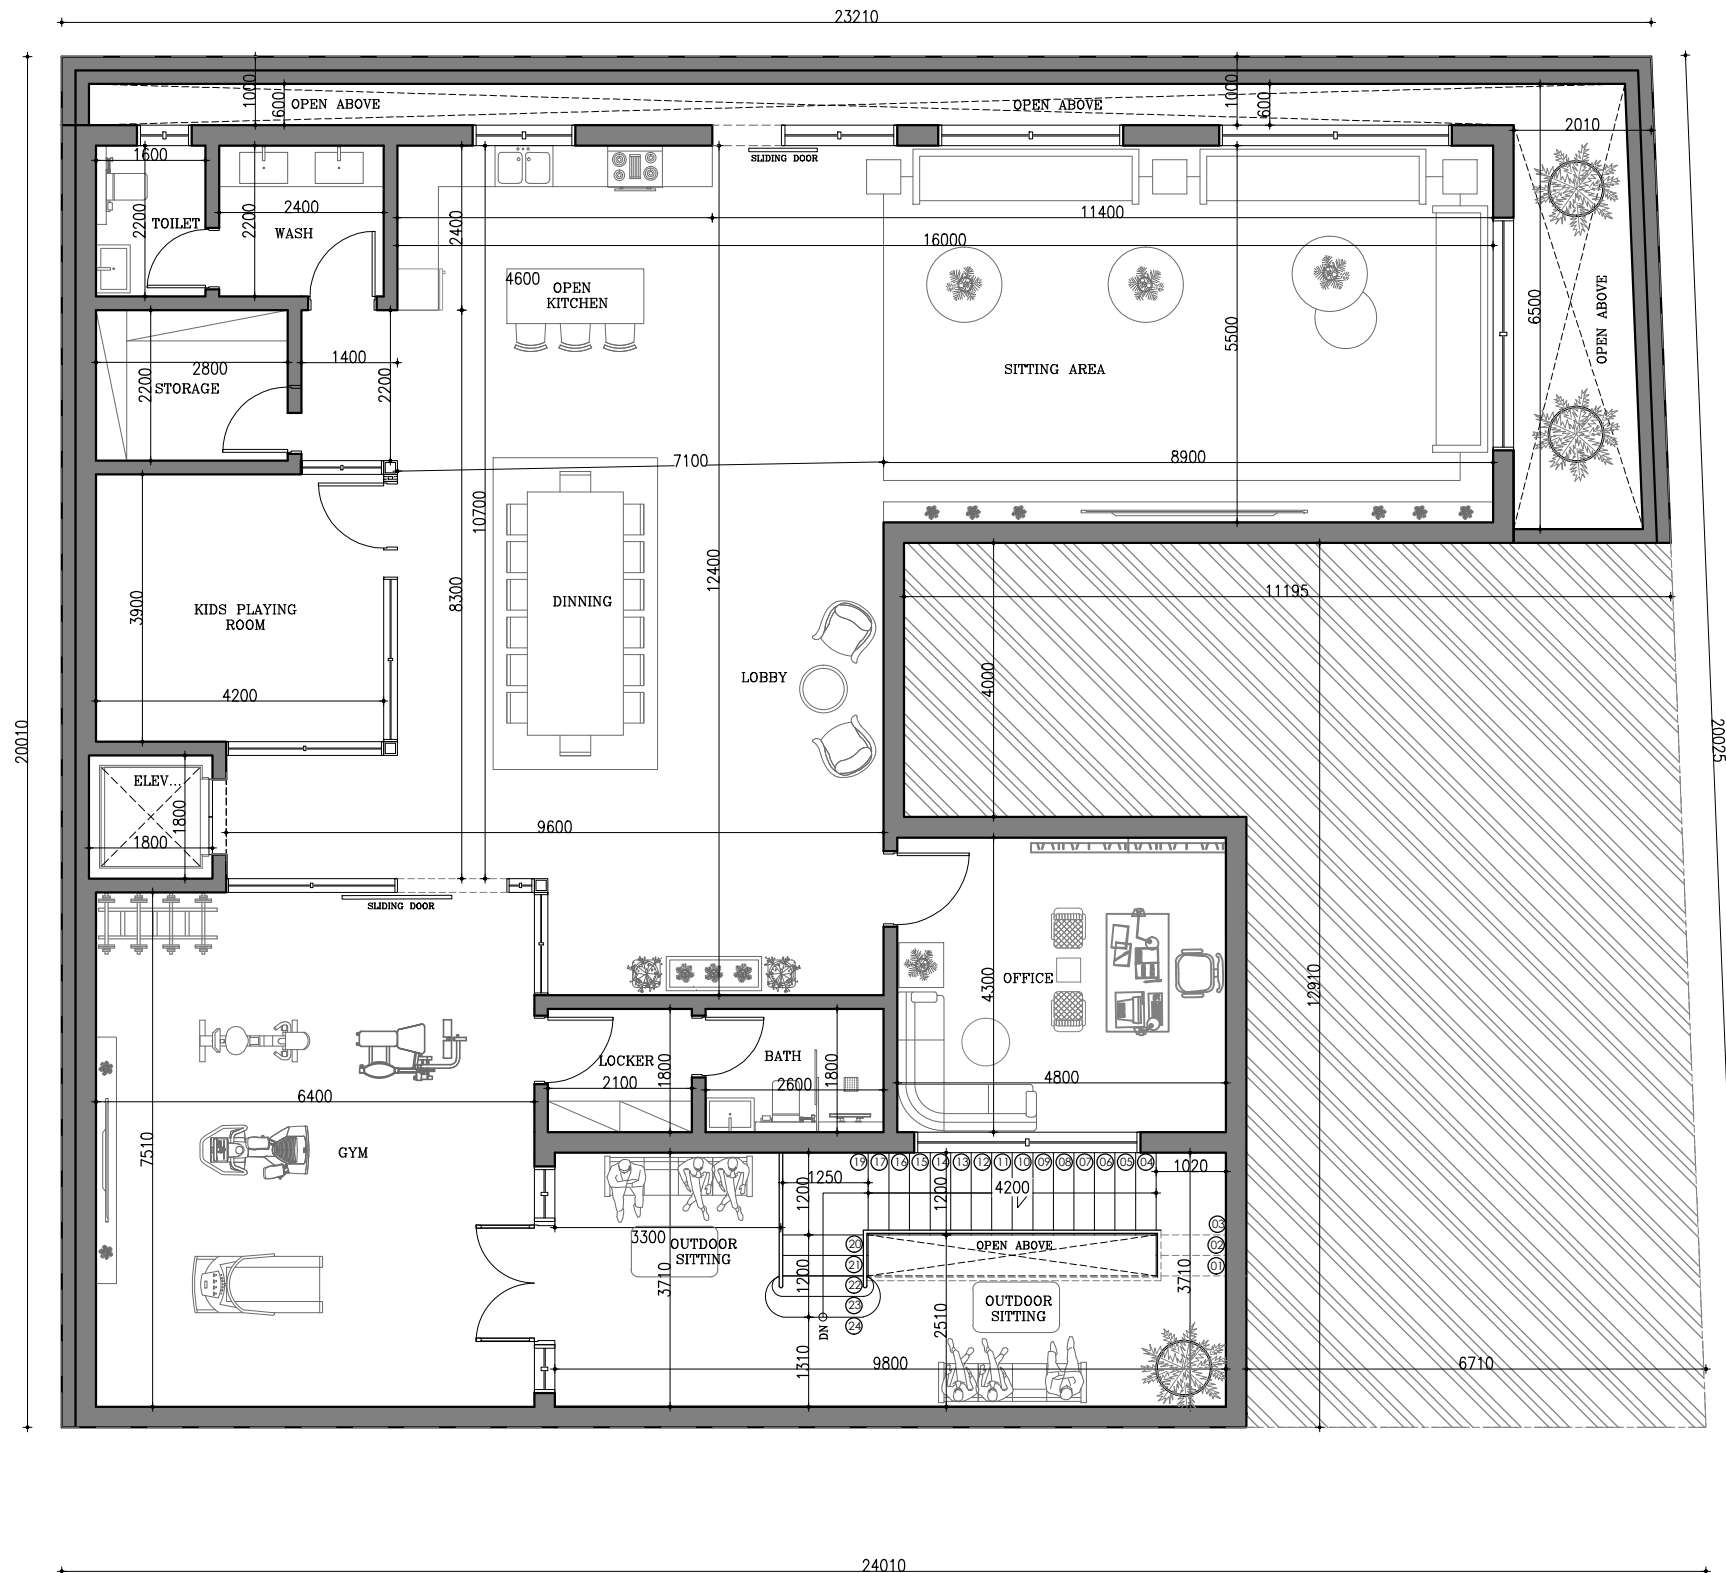

NORTH STREET 15 M

BASEMENT FLOOR PLAN

